


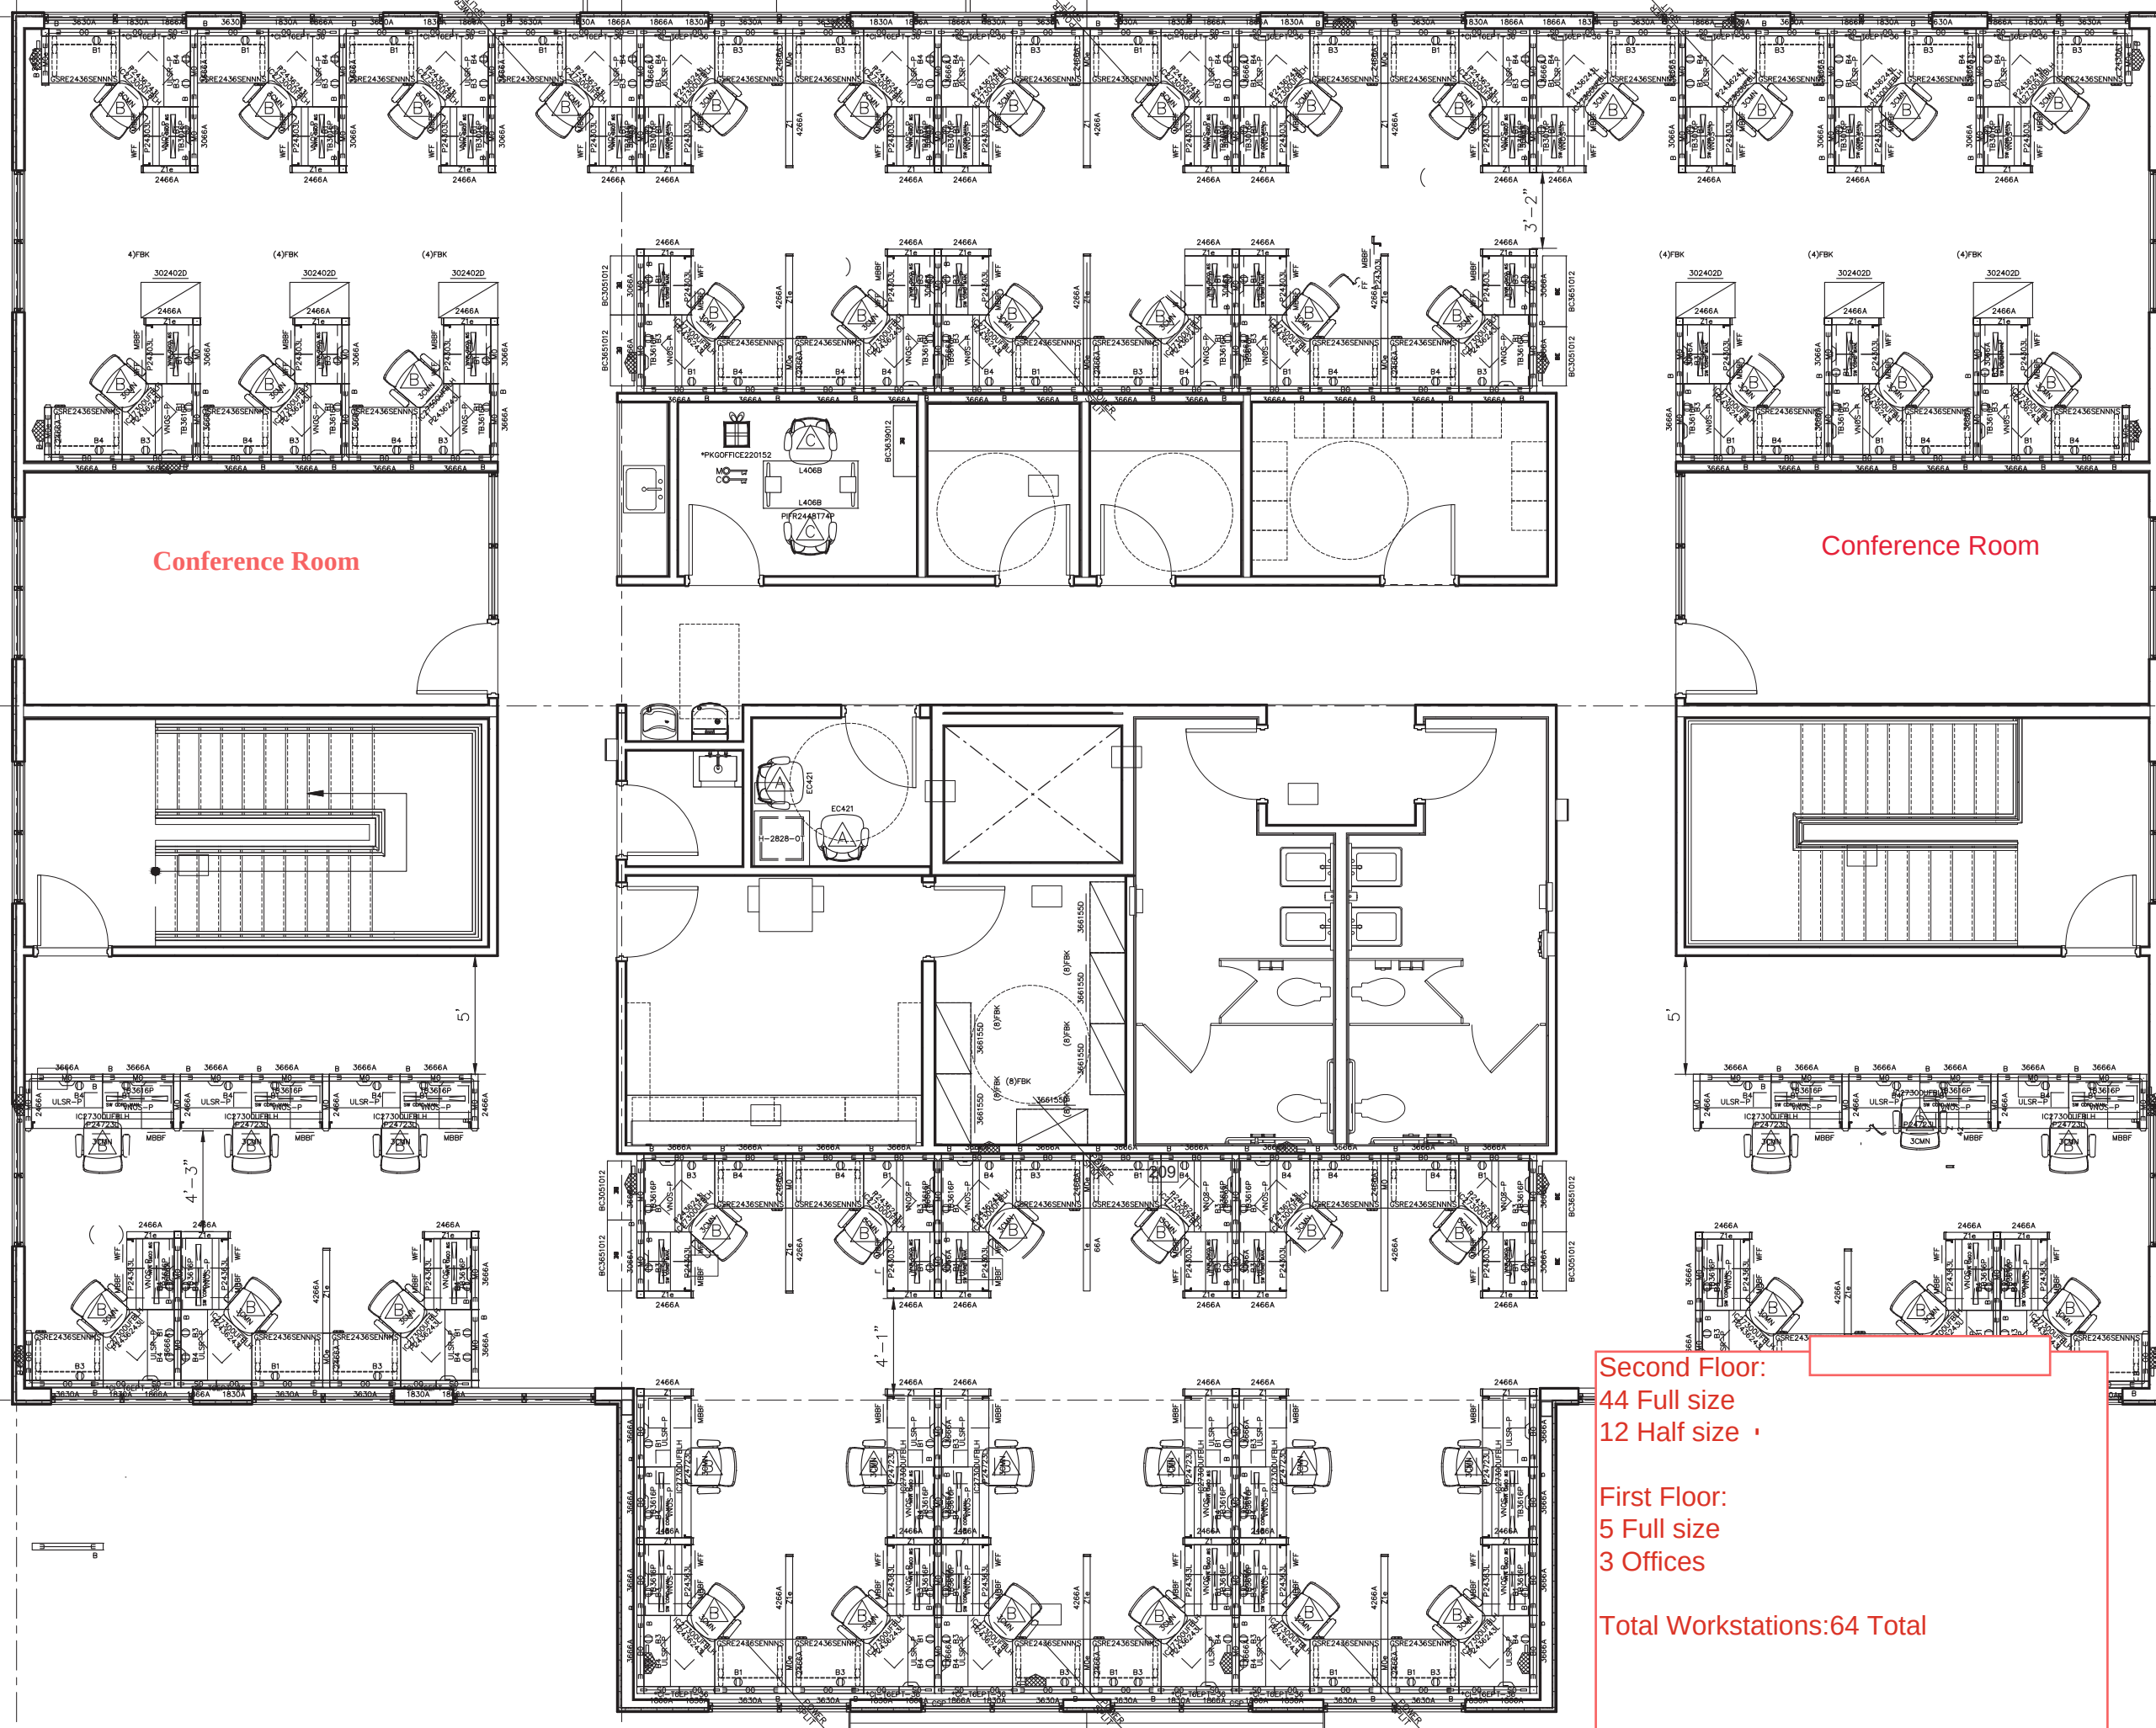

Conference Room

Conference Room

Second Floor:
44 Full size
12 Half size

First Floor:
5 Full size
3 Offices

Total Workstations: 64 Total

